



ЛИСТ 1. ПЕРЕДНИЙ ТОРЦЕВОЙ УЗЕЛ — СБОРКА И ПРОДОЛЬНЫЙ РАЗРЕЗ


Главный вид — разрез А-А одного цилиндра. Второй цилиндр имеет независимый аналогичный узел.

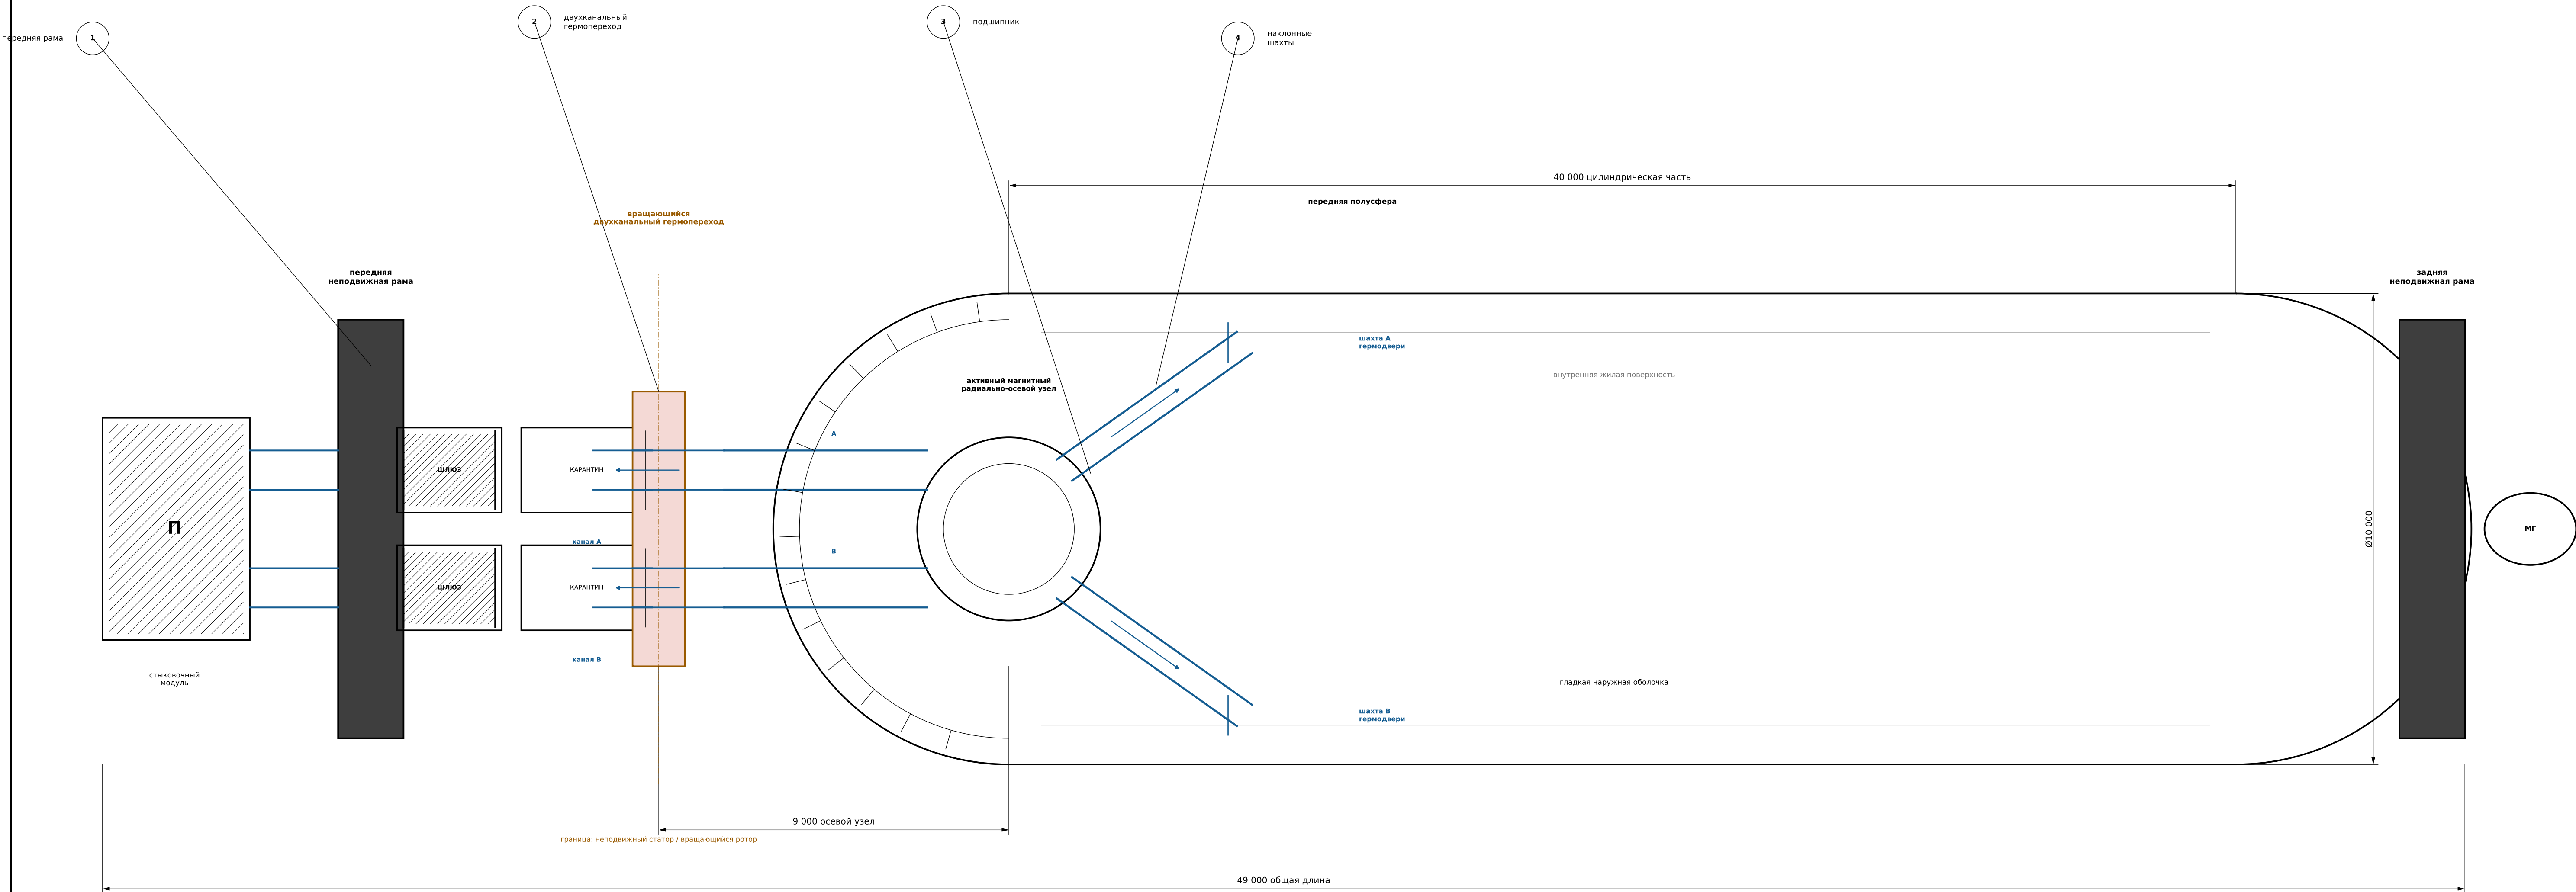

Б. ФРОНТАЛЬНЫЙ ВИД РАМЫ

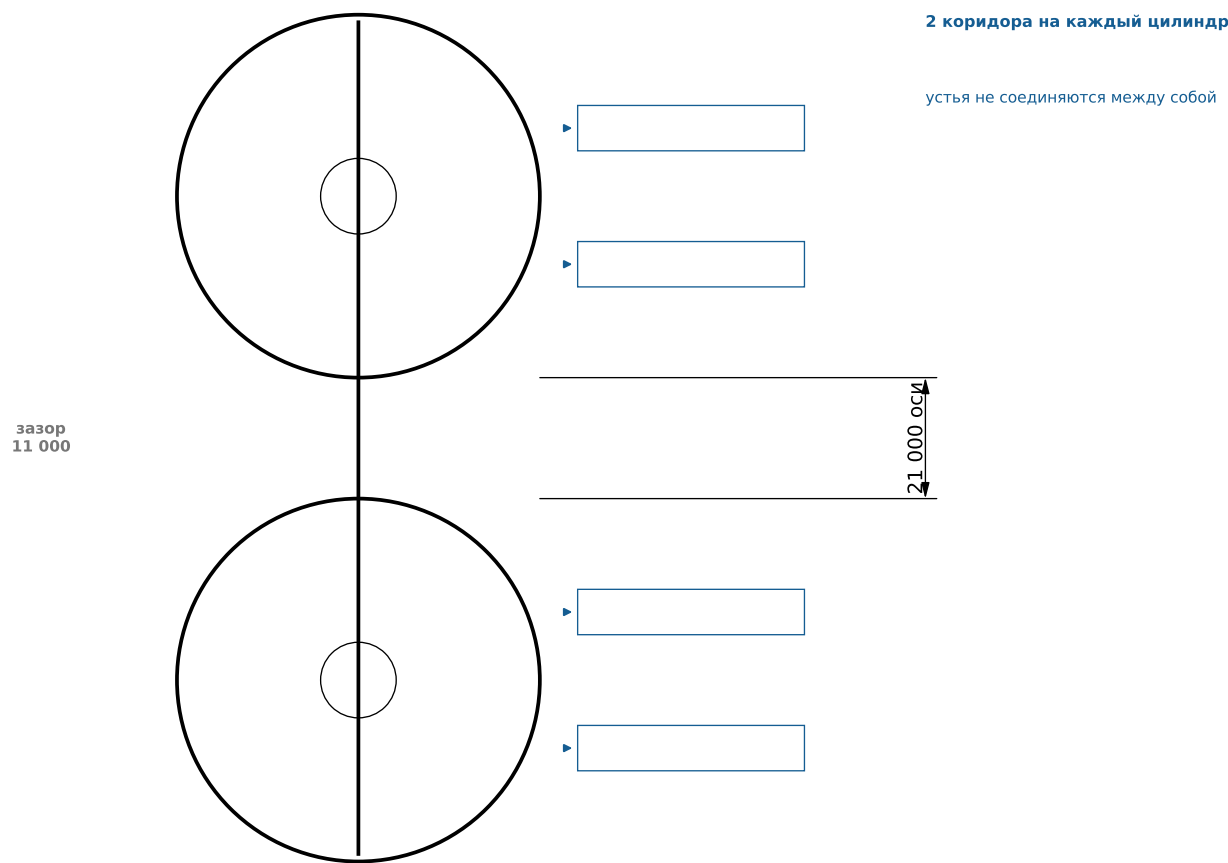

В. ПЛАН КОРИДОРОВ В ПЕРЕДНЕМ УЗЛЕ

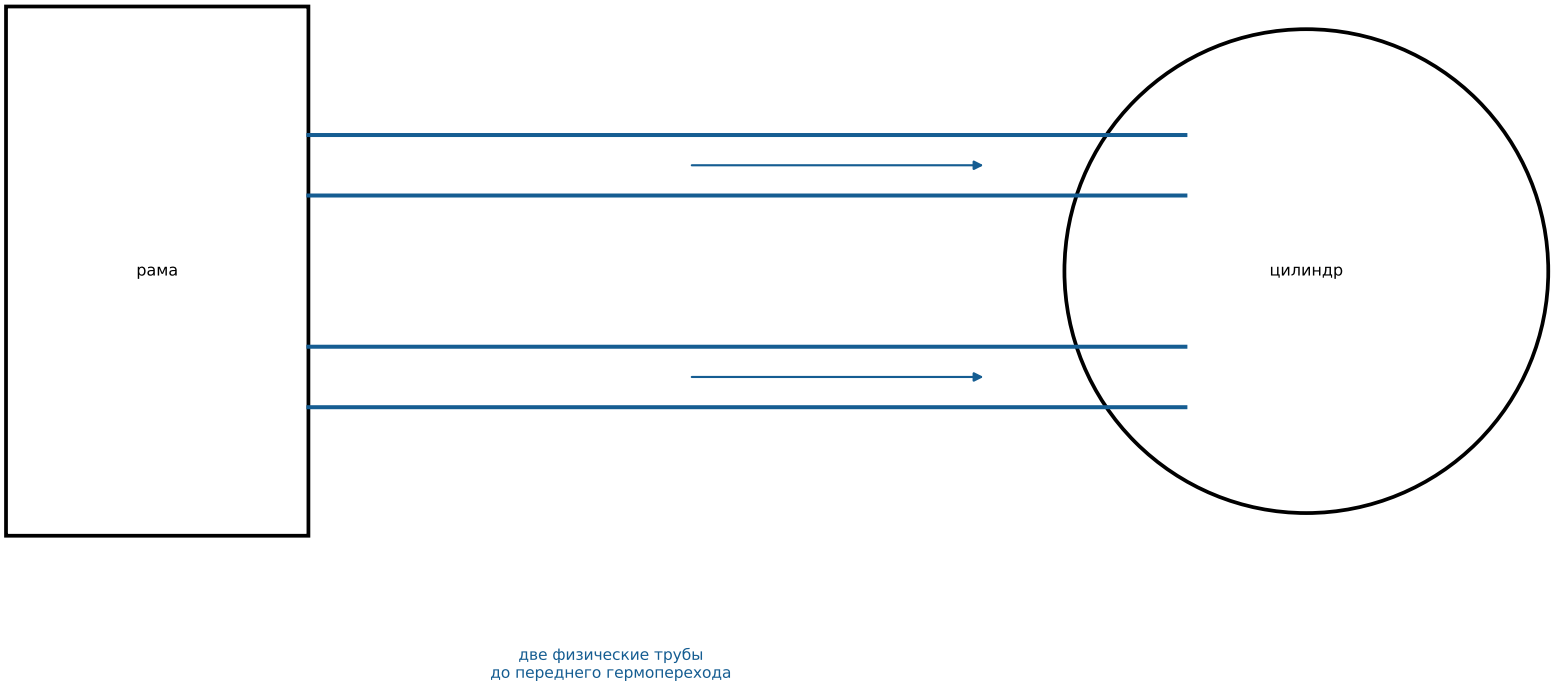


					ММОСО.01.930 СБ														
					Передний торцевой узел.														
Изм.		Лист		№ докум.		Подп.		Дата		Сборочный чертёж Масштаб									
Разраб.				Бугаенко Р. С.				10.09.2024		П				—	см. виды				
Пров.				НИК				10.09.2024											
Холтр.																			
Контр.				НИК				10.09.2024											
Утв.																			
										Лист 1		Листов 3				МХ «КРЯК» ММОСО'Н Сталь 18N(300)			


ЛИСТ 2. ДЕТАЛИРОВКА ТРАНСПОРТНОГО КОРИДОРА И ПОДШИПНИКОВОГО УЗЛА

Разрезы показывают реальные стенки, гермодвери, вал и опорные элементы; стрелки только указывают направление движения.

А-А. ПРОДОЛЬНЫЙ РАЗРЕЗ КОРИДОРА ЧЕРЕЗ ГЕРМОПЕРЕХОД

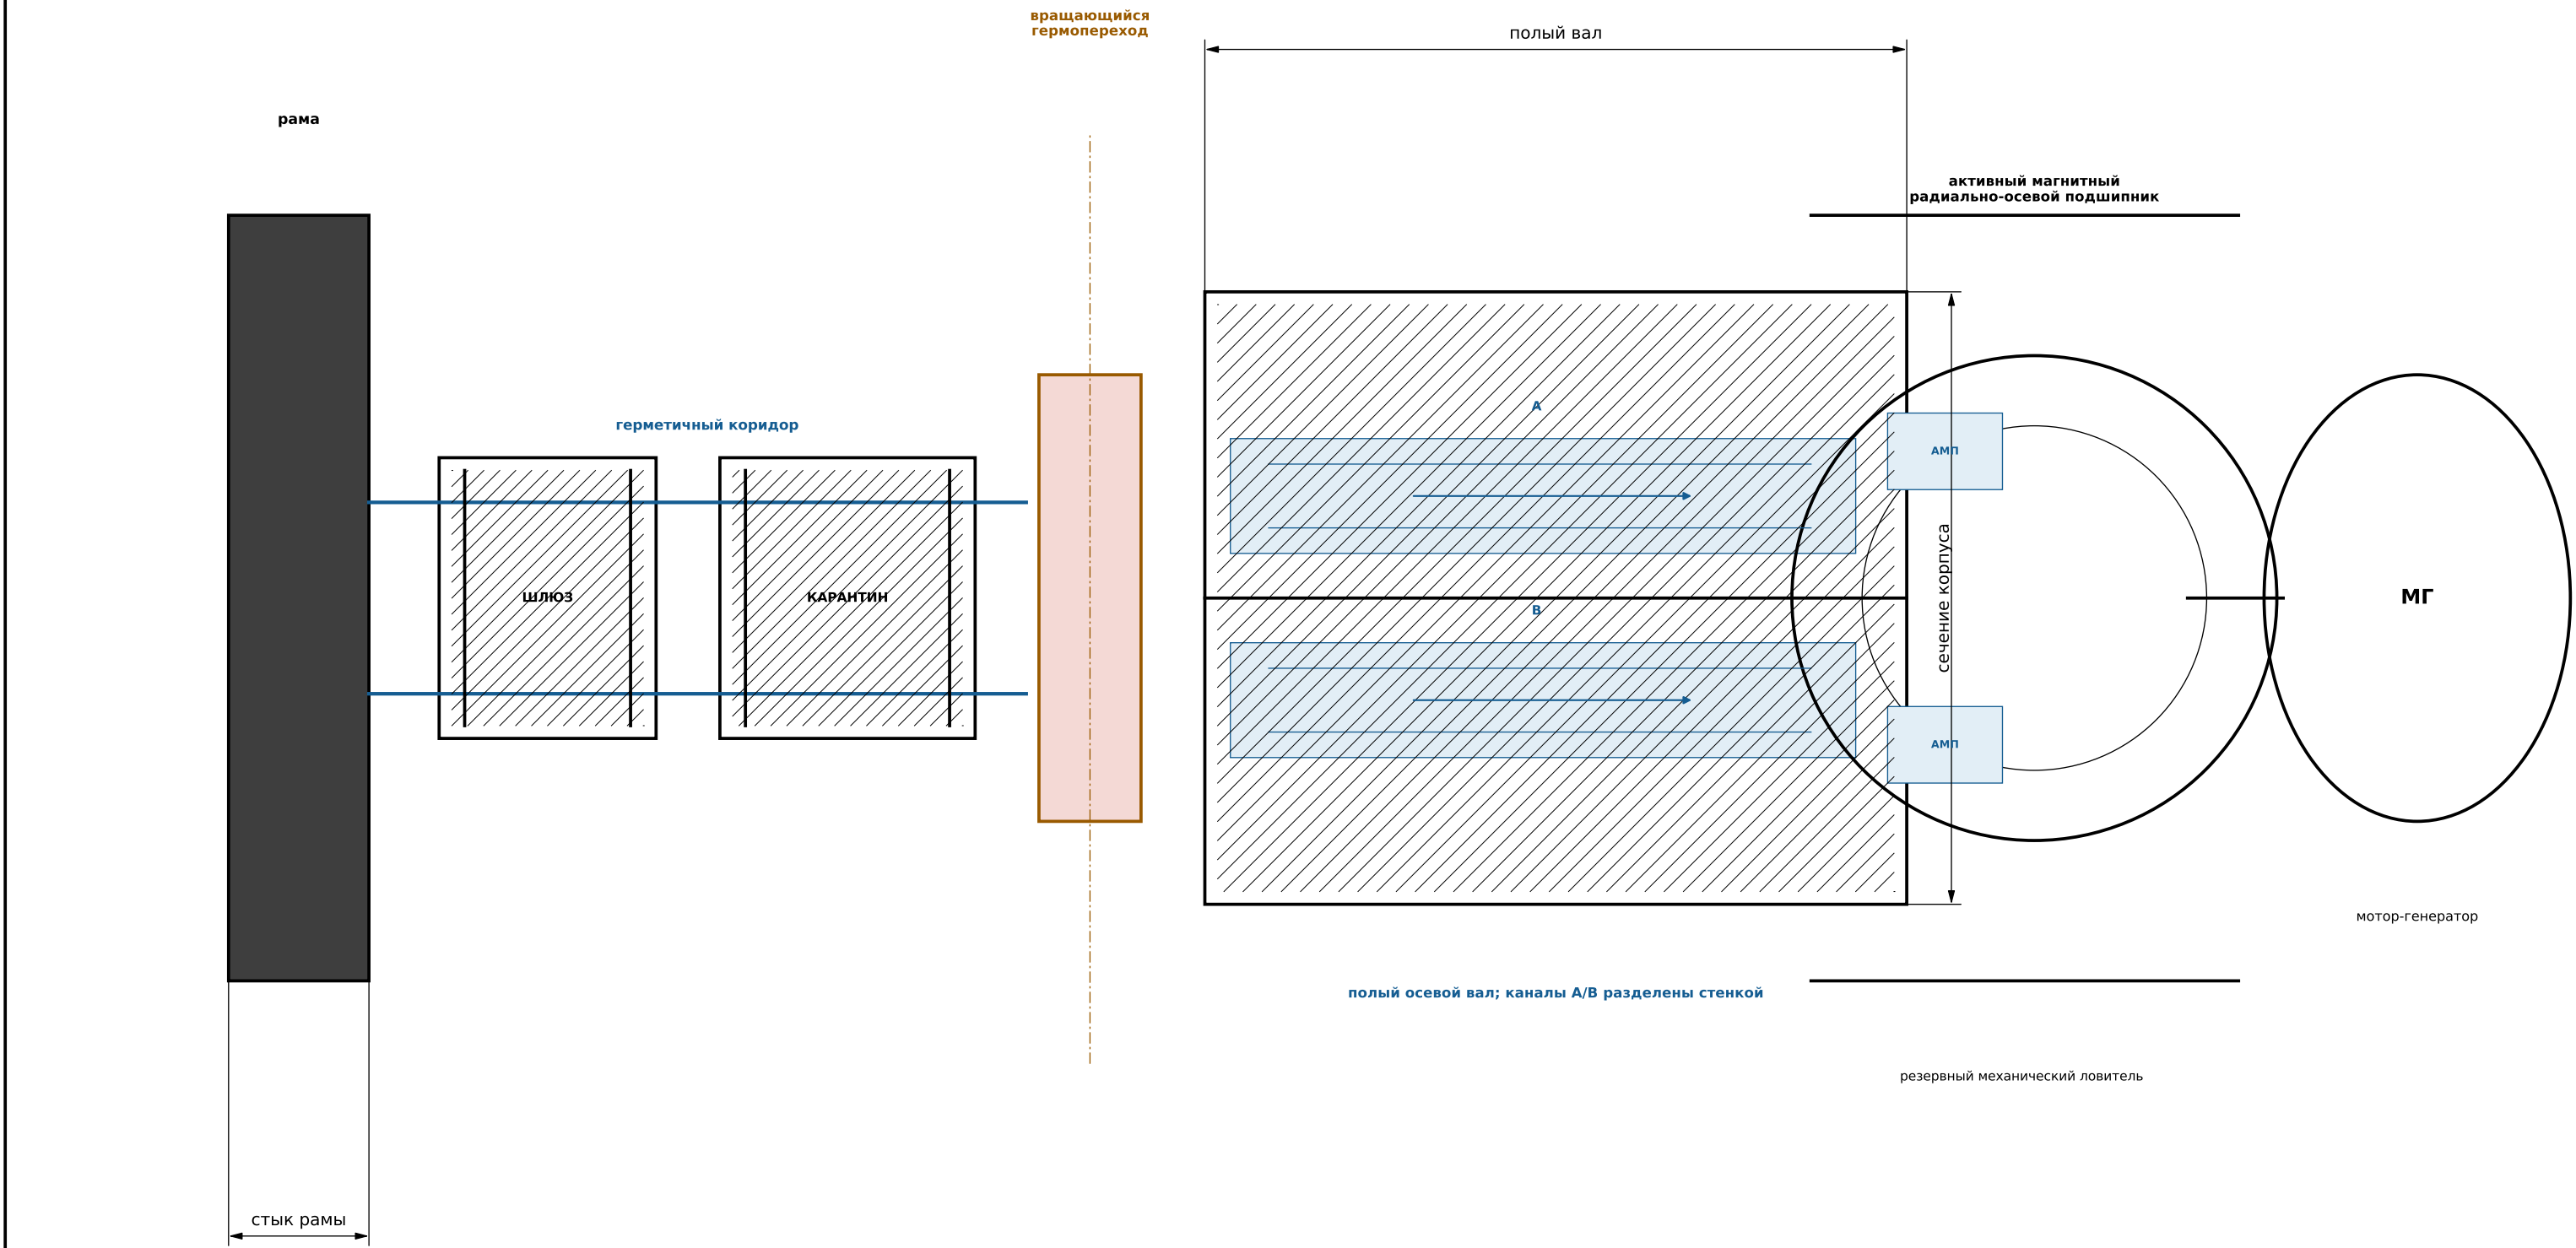


Б. ОСЕВОЙ РАЗРЕЗ ОПОРЫ (увеличено)

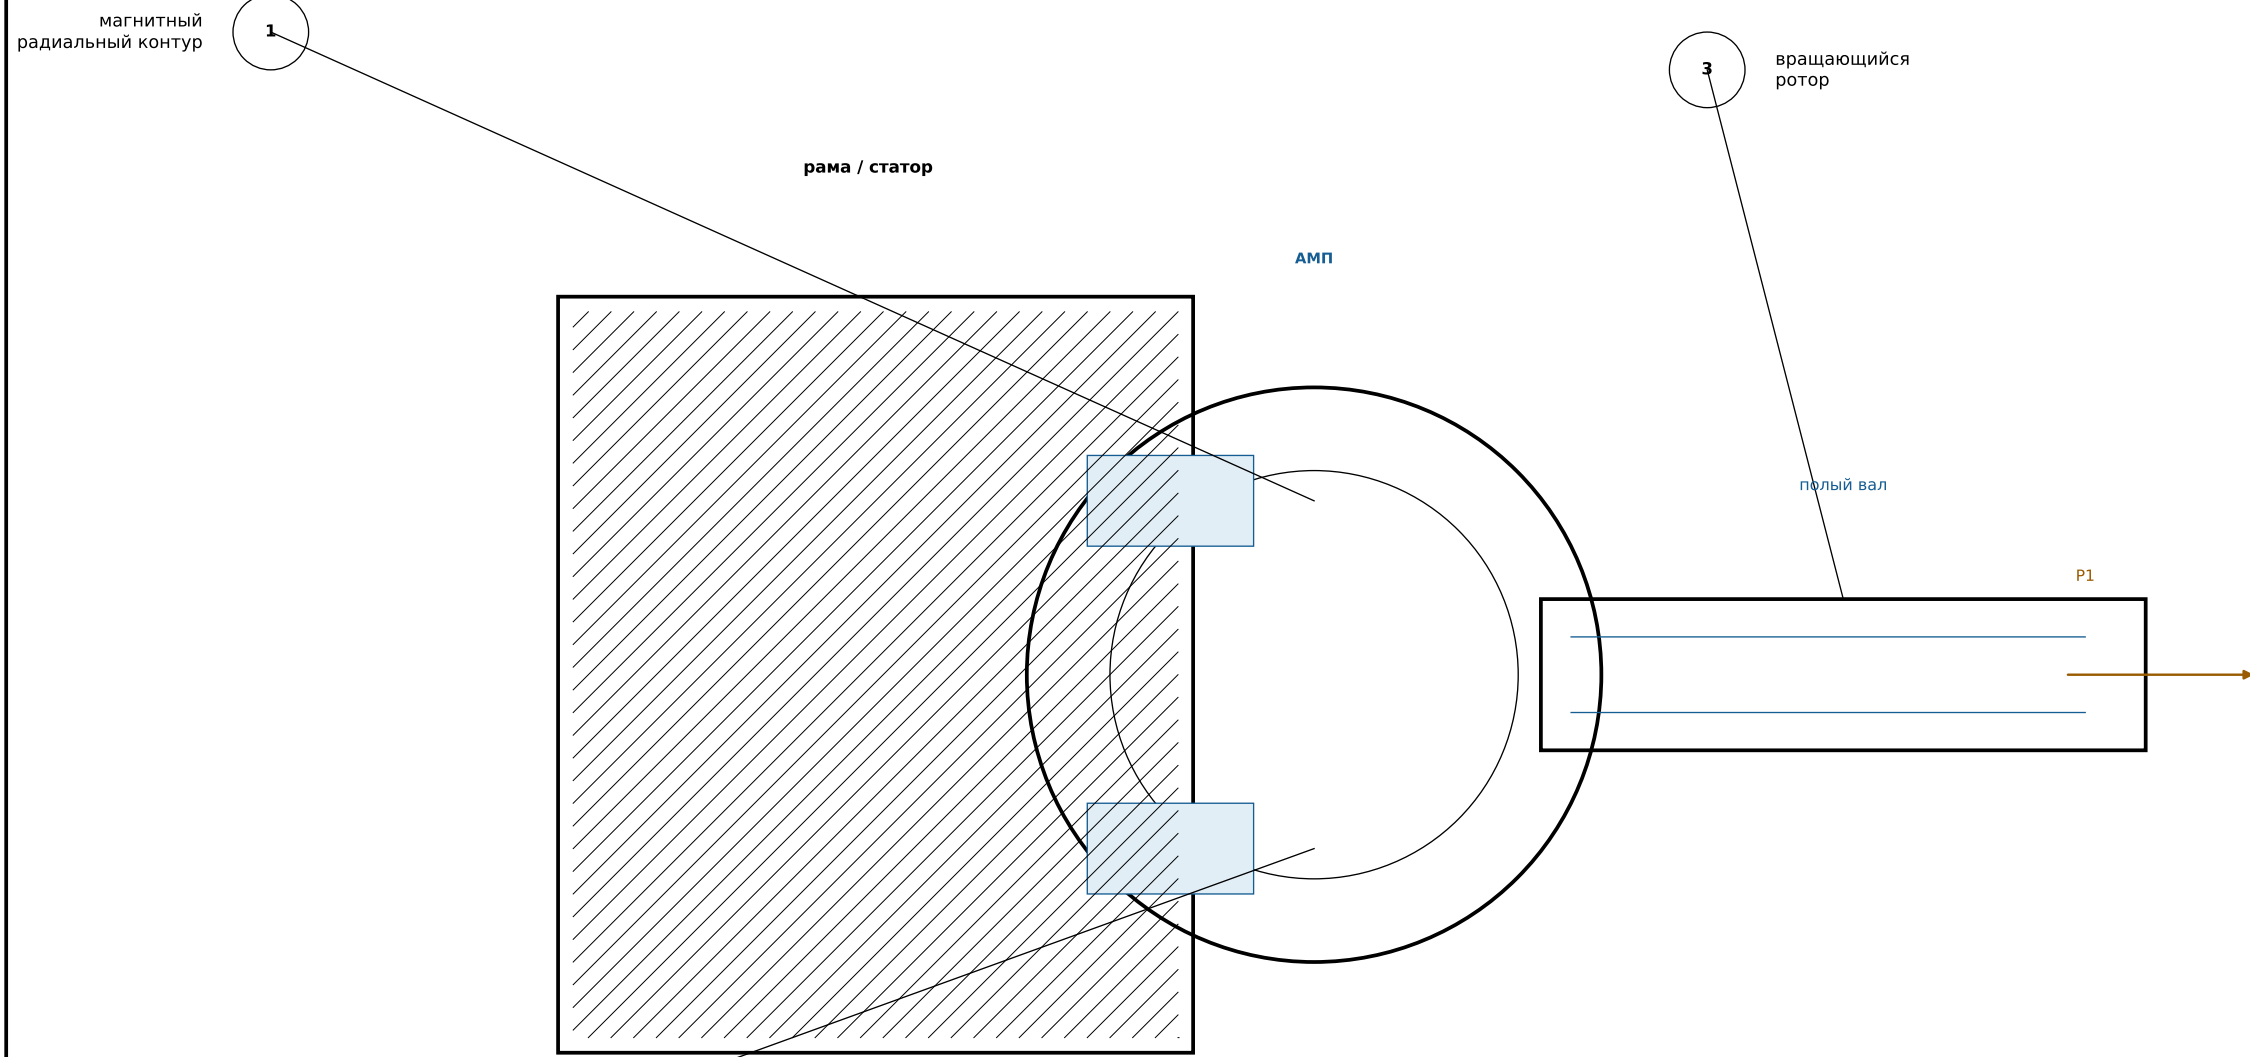


Все показанные каналы — физические замкнутые объемы с двумя стенками. магнитным контуром просвета коридора и шахты должен быть назначен отдельным расчетом вместимости; этот контур фиксирует геометрию, последовательность узлов и границы герметизации.

В. СЕЧЕНИЕ СЕКЦИОННОЙ ГЕРМОДВЕРИ

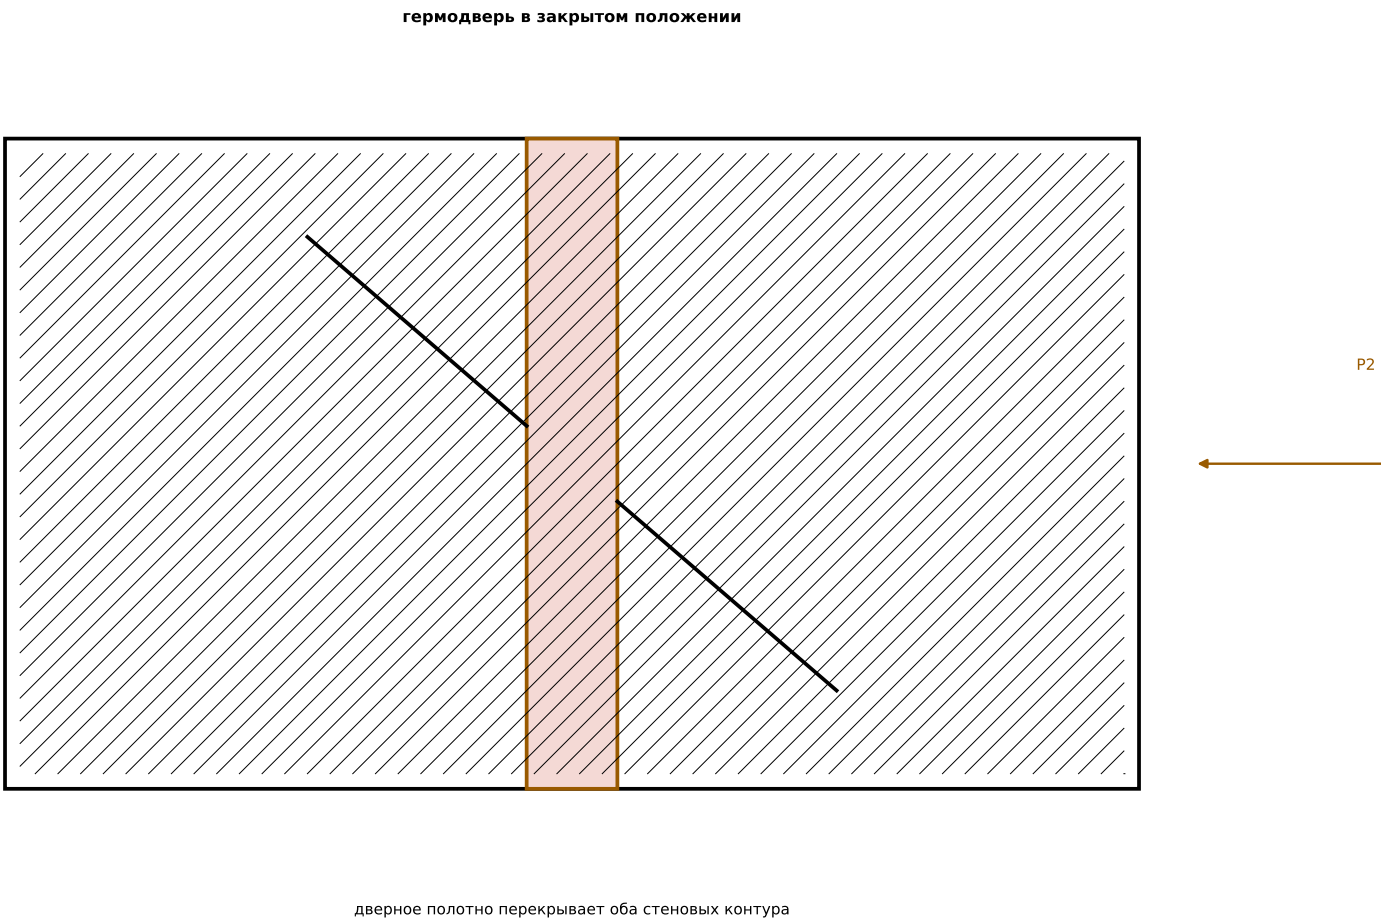


Г. СЕЧЕНИЕ НАКЛОННОЙ ШАХТЫ

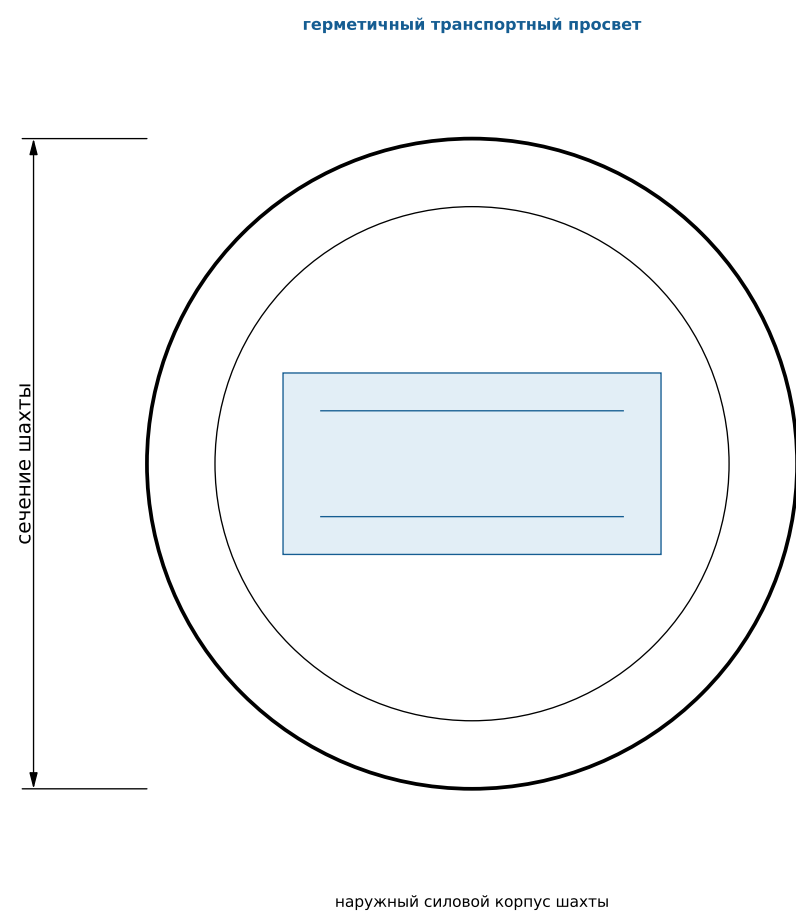


					ММОСО.01.940 СБ					
					Транспортный коридор.					
					Деталировка и сечения					
Изм.	Лист	№ докум.	Подп.	Дата	Лит. Масса					
					Масштаб					
Разраб.		Бугаенко Р. С.		10.09.2024	П			—	СМ. ВИДЫ	
Пров.		НИК		10.09.2024						
Холтр.										
Холтр.		НИК		10.09.2024						
Утв.					Лист 2			Листов 3		МХ «КРЯК» ММОСО'Н
										Сталь 18Ni(300) / YBCO

ЛИСТ 3. ЦИЛИНДР — ПЕРЕДНЯЯ ПОЛУСФЕРА, ШАХТЫ И ВЫХОД НА ЖИЛУЮ ПОВЕРХНОСТЬ

Разрез показывает внутреннюю геометрию вращающейся передней полусферы; внешняя оболочка остаётся гладкой.

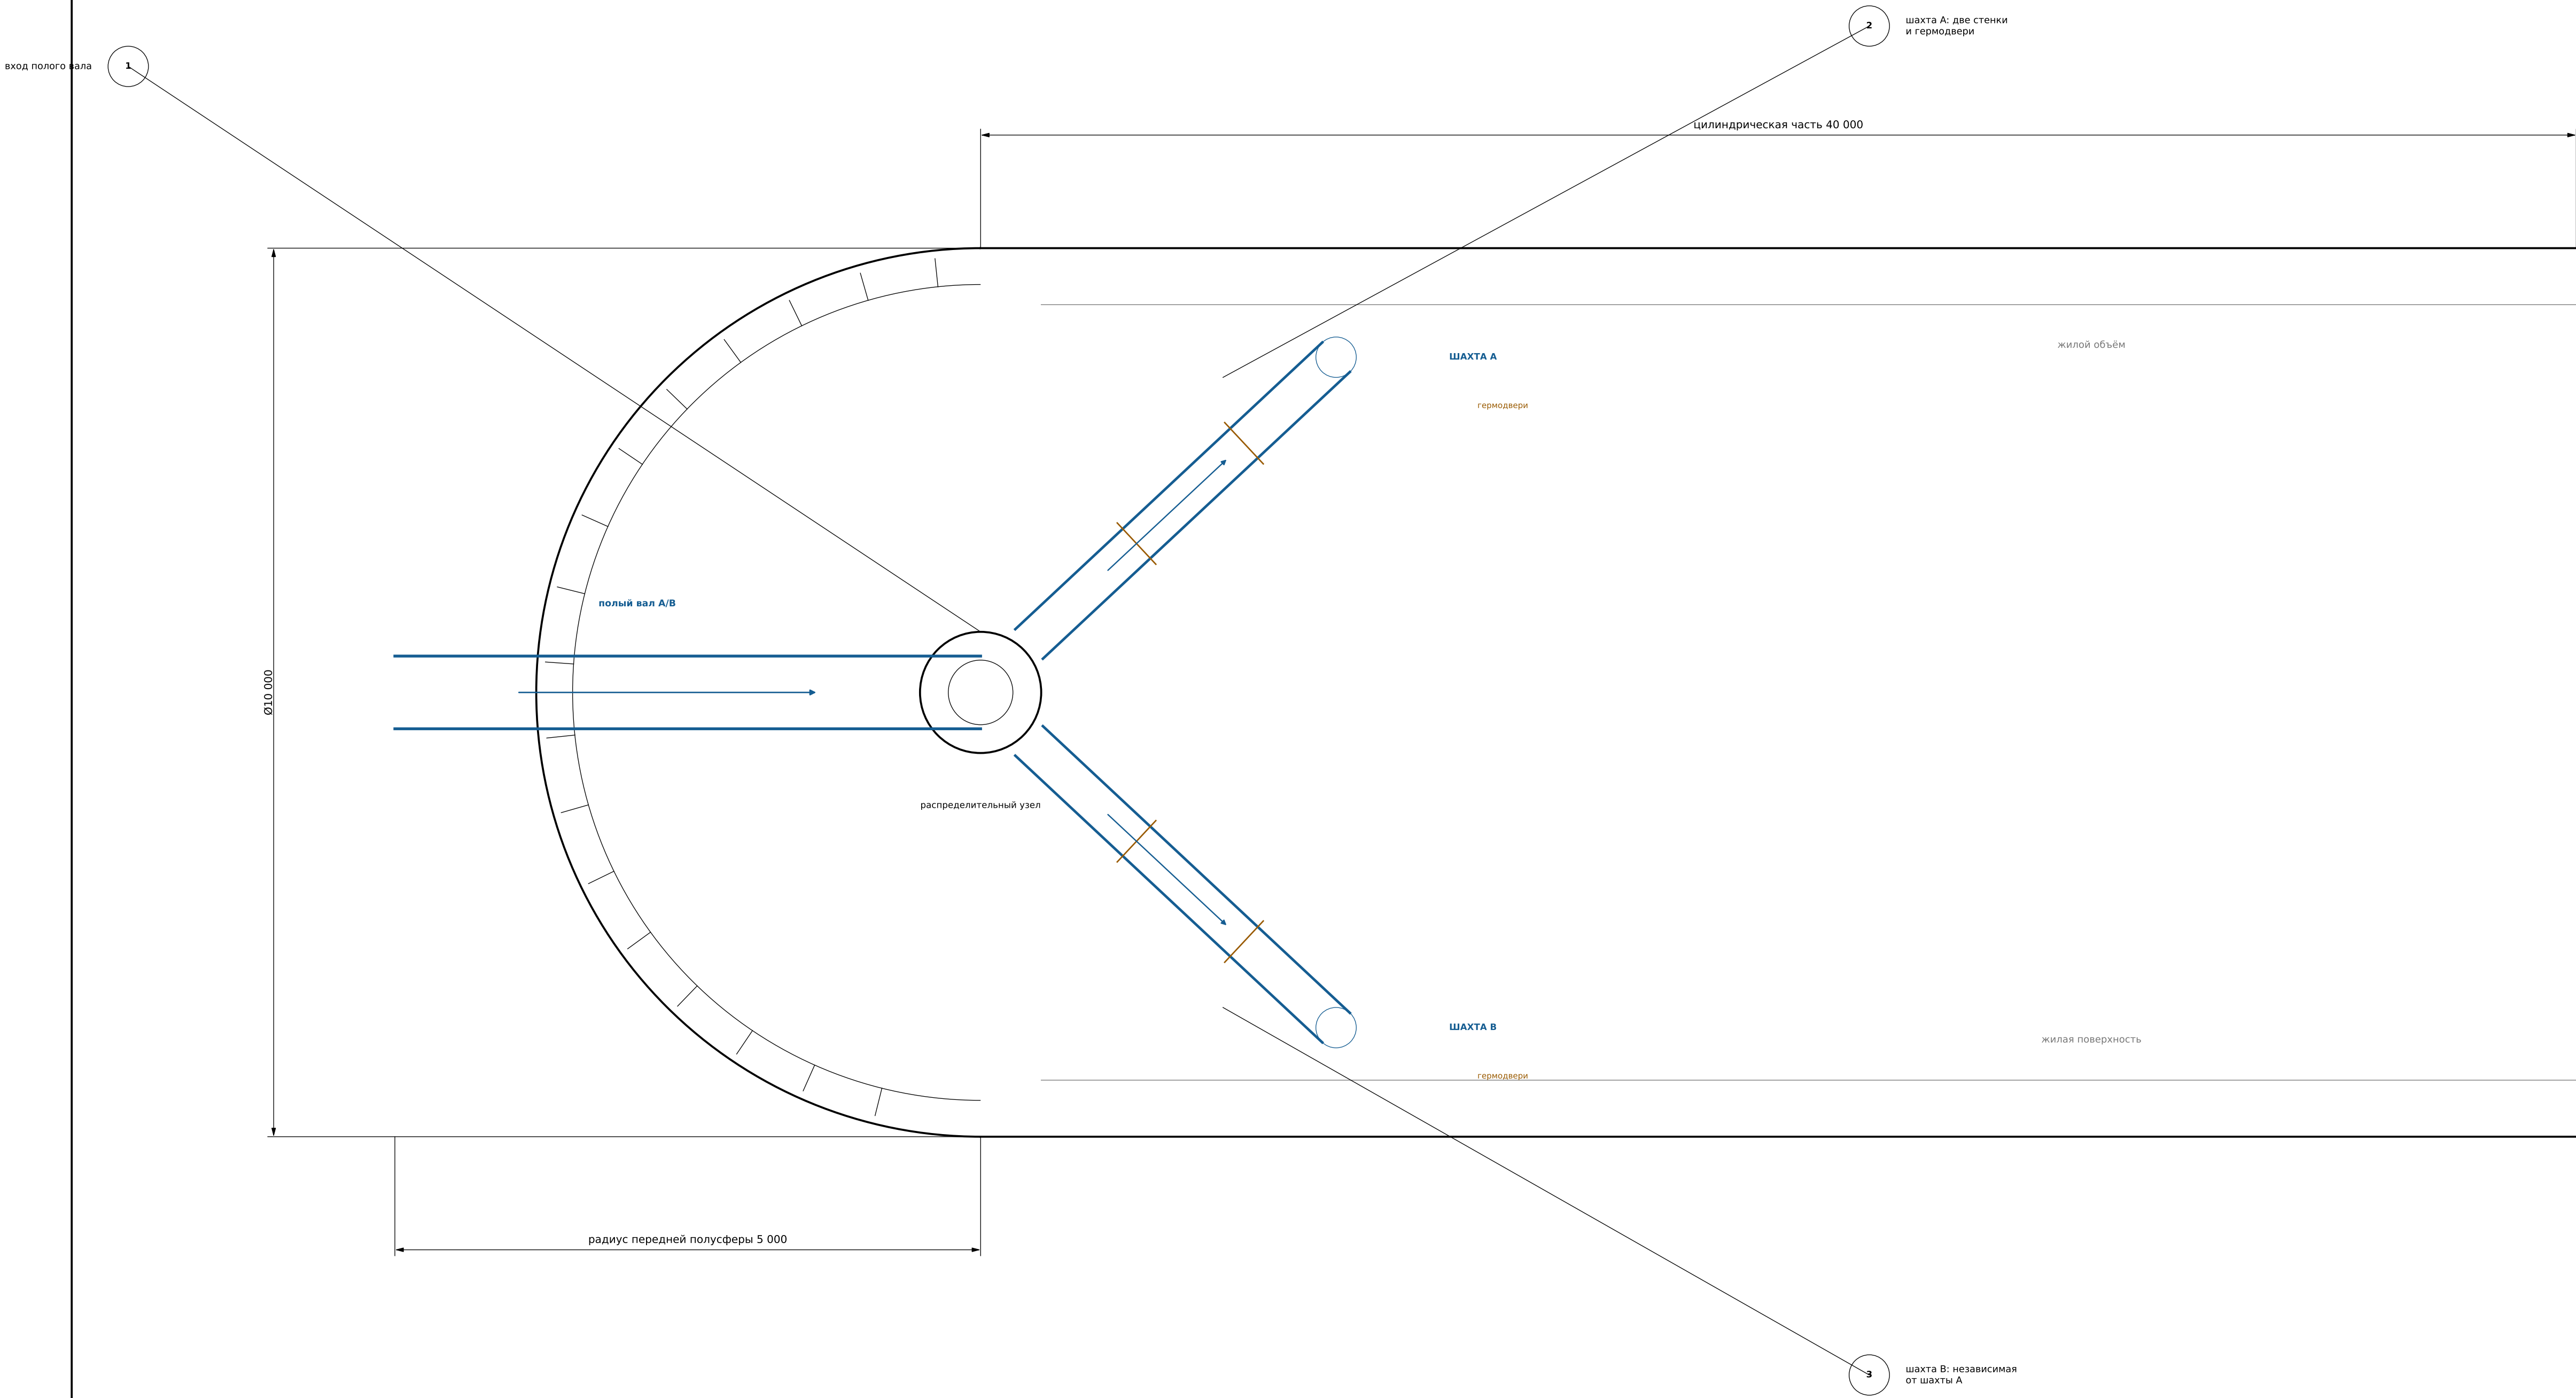


Б. ПОПЕРЕЧНЫЙ ВИД ПЕРЕДНЕЙ ПОЛУСФЕРЫ

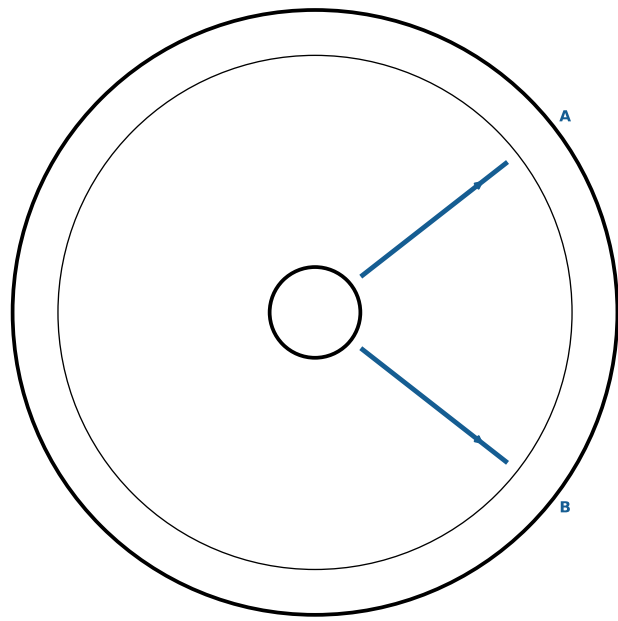

две шахты на передней полусфере

В. ВЫХОД ШАХТЫ В ВЕСТИБУЛЬ — СЕЧЕНИЕ

гермодверь выхода

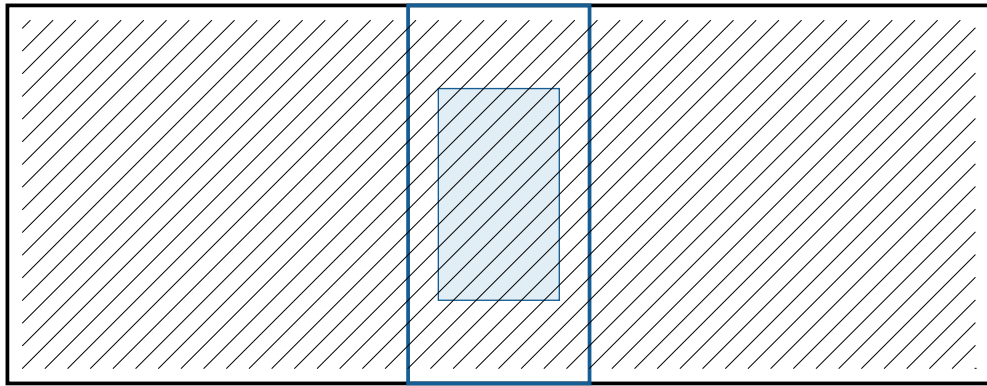

вестибиль → жилой объём

Трасса в полусфере
1. Вал приходит к распределительному узлу.
2. Каналы A/B расходятся в две шахты.
3. В каждой шахте есть секционные двери.
4. Выходы ведут в разные вестибли.
5. В межцилиндровый зазор трасса не выходит.

					ММОСО.01.950 СБ				
					Цилиндр.				
Изм.	Лист	№ докум.	Подп.	Дата	Передняя полусфера и выходы шахт				
					Лит.	Масса	Масштаб		
Разраб.		Бугаенко Р. С.		30.09.2024	П		—	см. виды	
Пров.		НИК		30.09.2024					
Холтр.									
Н.контр.		НИК		30.09.2024					
Утв.									
					Лист 3		Листов 3		МХ «КРЯК» ММОСО'Н Сталь 18Ni(300)